

ENERGIATANÚSÍTÁS
FELMÉRŐLAP


2016.02.02


Adatok						Megjegyzés/Érték
Alapadatok:						Fotók
Tanúsítás időpontja:						külső, 4 oldali
Megrendelő neve:						hőleadó
Megrendelő címe:						ablak
Telefonszám:						kazán
Épület címe:						megújuló
Épület HRSZ:						belső szig (káva)
Épület építési éve:						belső sz fal-födém
Felújítás éve						
Fűtött szintek száma						
Műemlék:						
Épületszerkezetek:	(belülről kifelé)					
Fal:	Födém:	Padló:	Padlás/tető	Ablak:	Egyéb:	
Épületgépészet						
Fűtés:						
Fűtés típusa:						
Fűtés energiahordozója:						
Kazán fűtött téren:	belül	kívül	nincs			
Vízhőmérséklet:	90/70	70/55	55/45	35/28		
Elosztó vezetékek:	belül	kívül	nincs			
Keringtetés energiaigénye:	ford.szám.szab.	állandó ford.szám.	nincs			
Hőlépcső:	20K	15K	10K	7K		
Hőleadók rendszere:	Kétcsöves	Egycsöves	Egyedi			
Szabályozás: kétcsöves rendszernél	Nincs	Egy központi	Term. Szelep	Elektr. Szab.	Elektr. Szab.+opt. Funkció	
Szabályozás egycsöves rendszernél	Egy központi	Időjárásfüggő központi szabályzó	Term. Szelep			
Termosztát külön:	van	nincs				
Hőtárolás:	belül	kívül	nincs			
Hőtárolás vízhőm.:	55/45	35/28				
HMV:						
HMV típusa:						
Energiahordozó:						
Tároló fűtött téren:	belül	kívül	nincs			
Elosztás:	cirkuláció nél	cirkulációval				
Elosztás:	belül	kívül				
Segédenergia:						
Korszerűsítés leírás:						

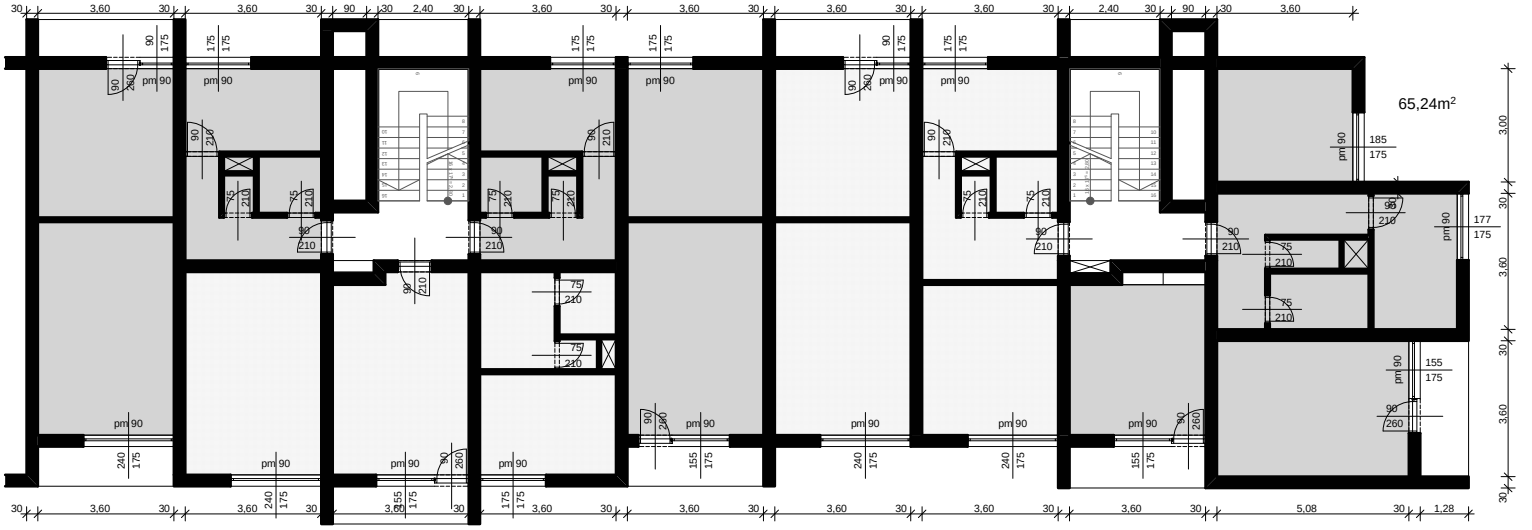


A típus

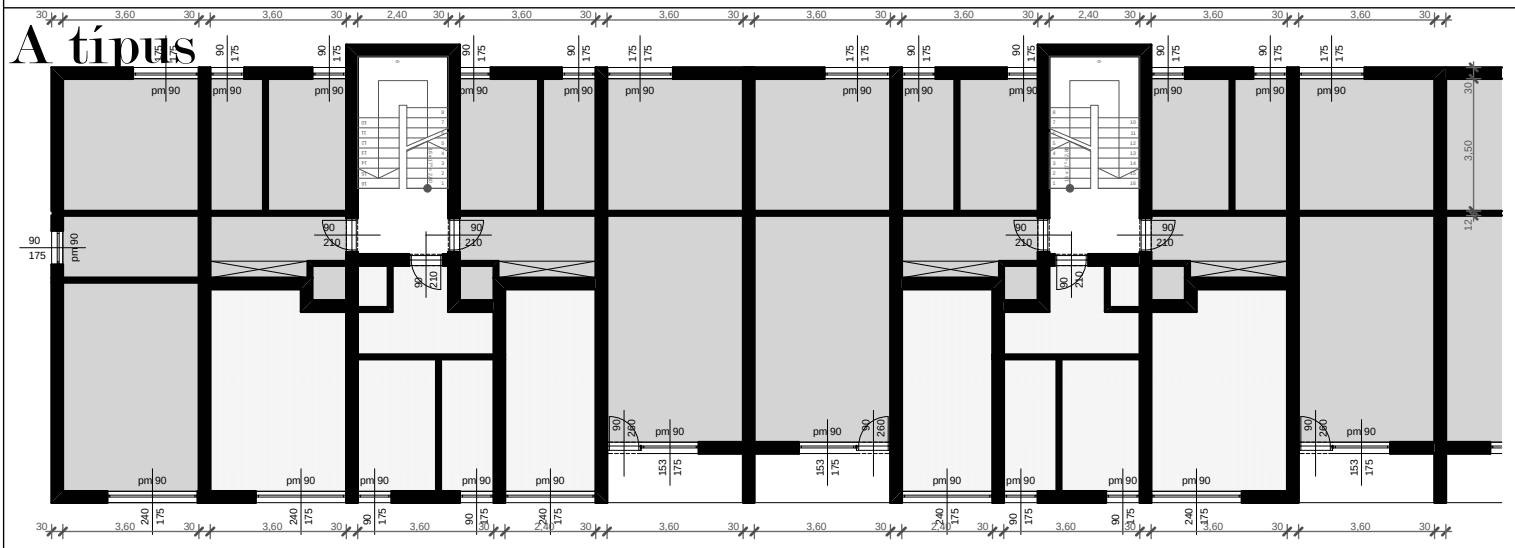

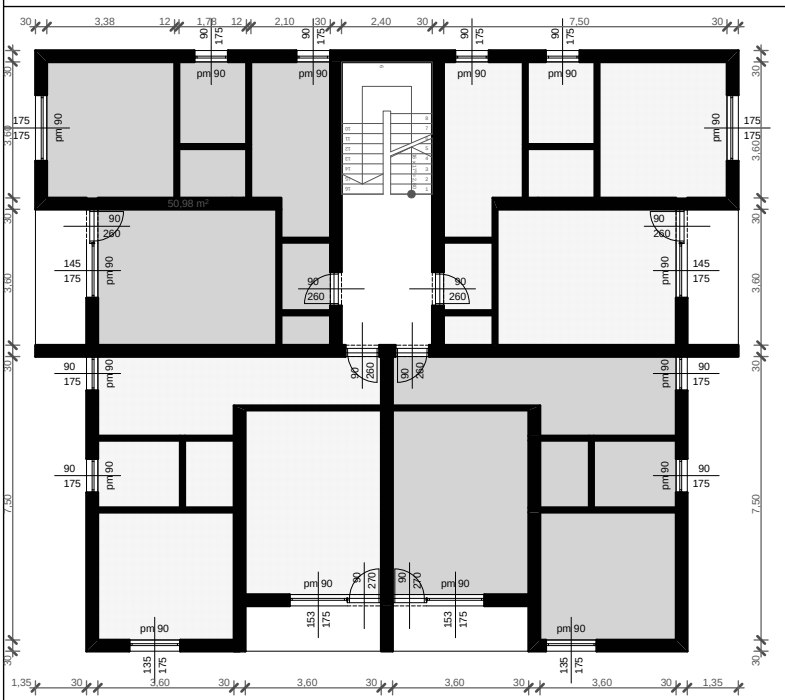

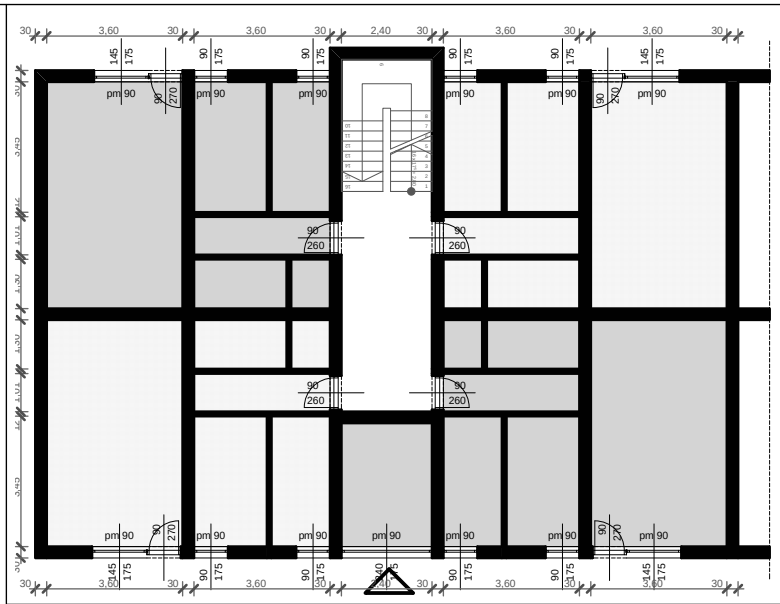

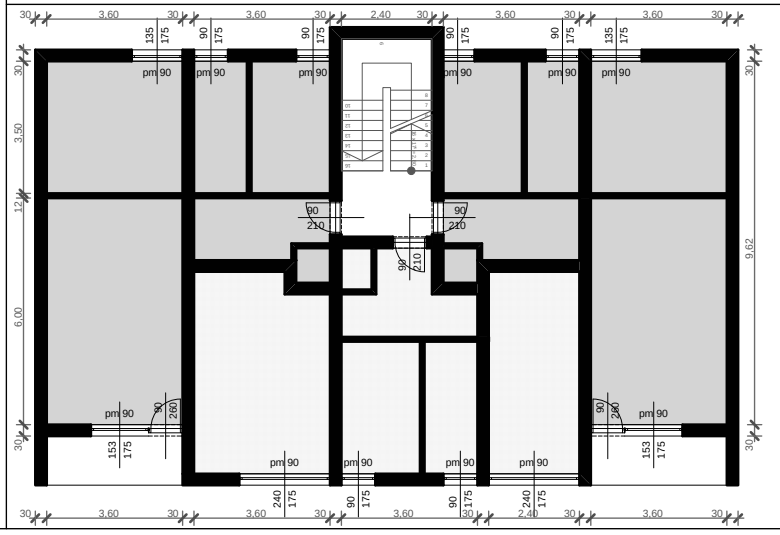

A típus

2 lh. A=2082,62 m2
V=4156,32 m3 A/V=0,50
3 lh. A=2981,08 m2
V=6171,30 m3 A/V=0,48
4 lh. A=3869,50 m2
V=8186,29 m3 A/V=0,47

Blokkos típusok: